
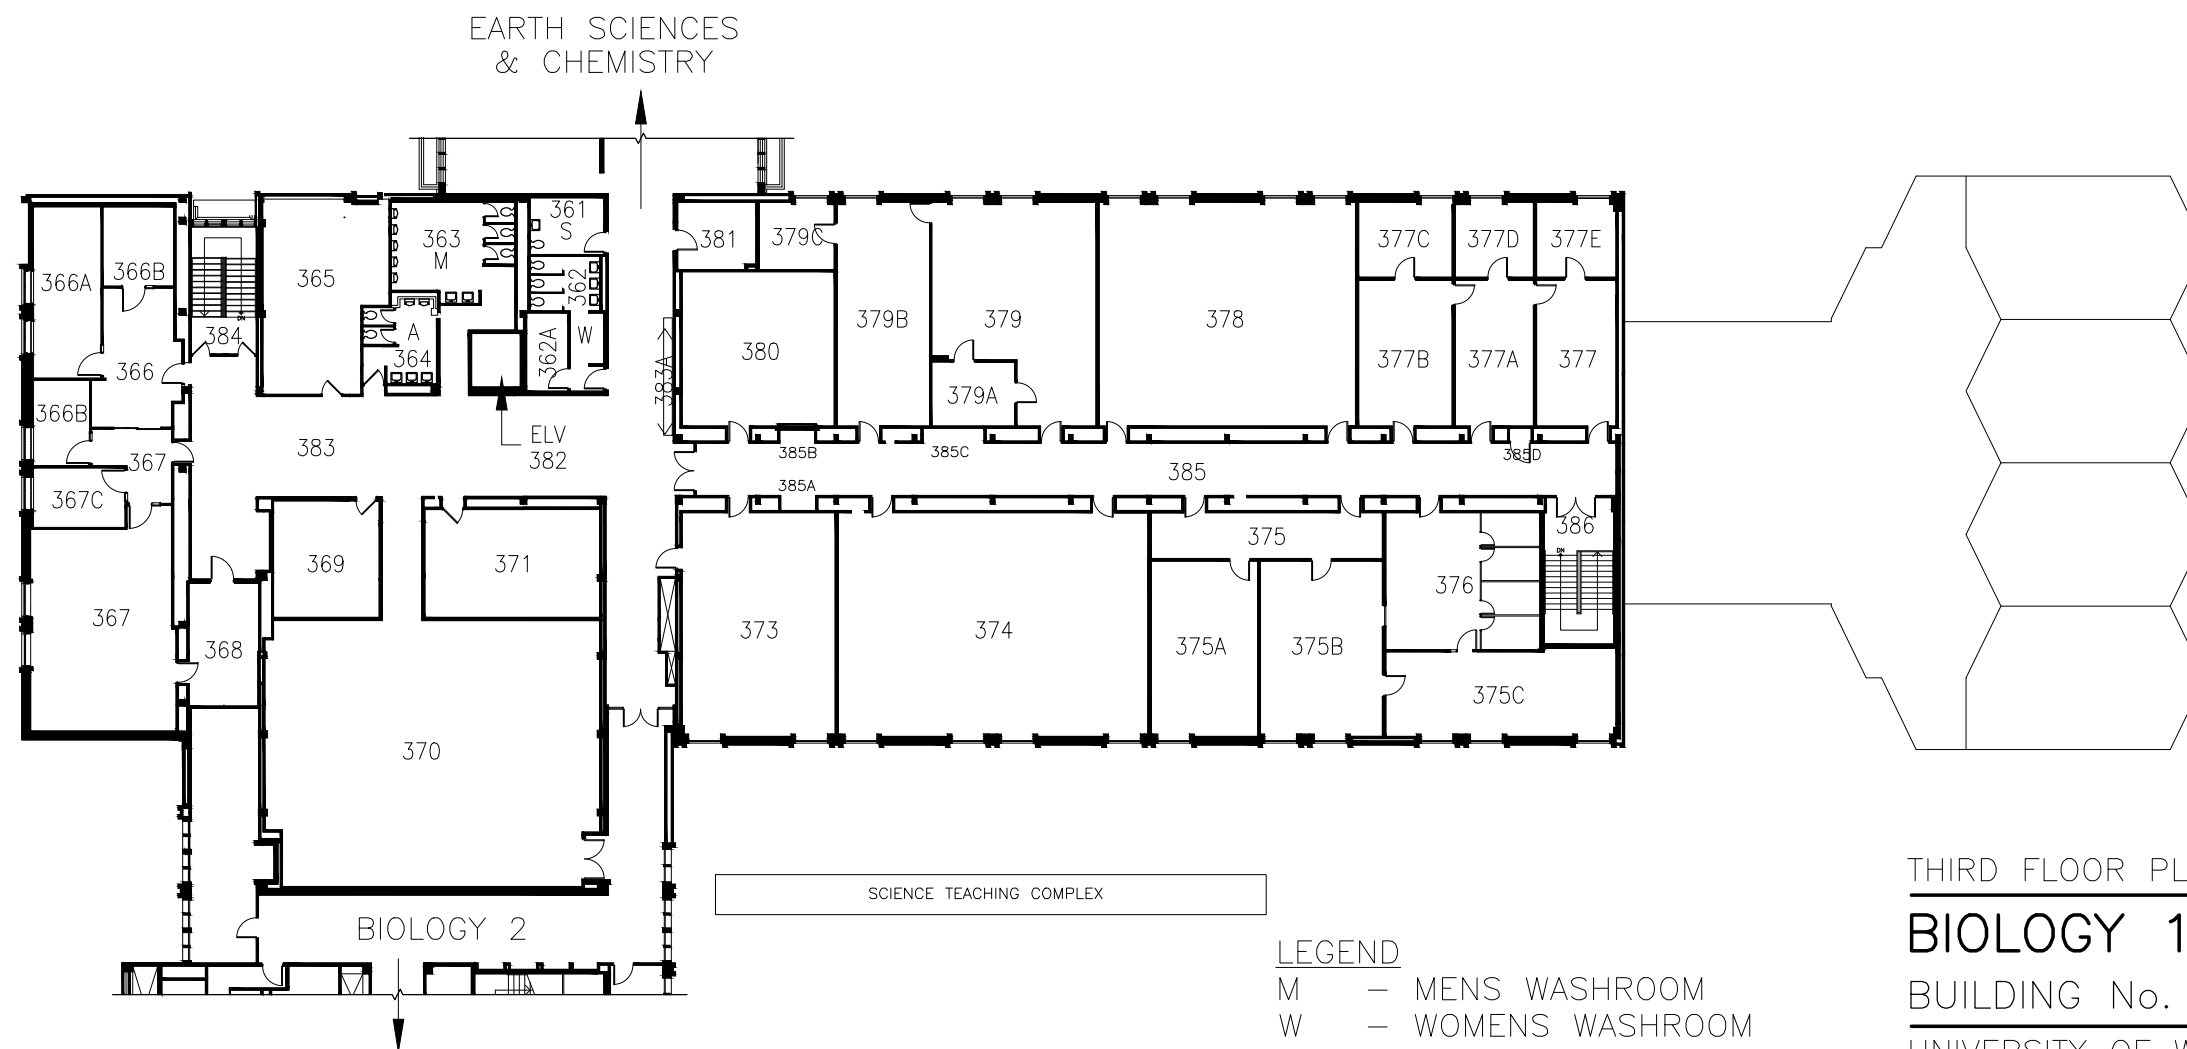
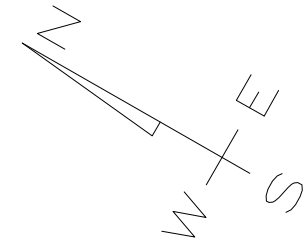
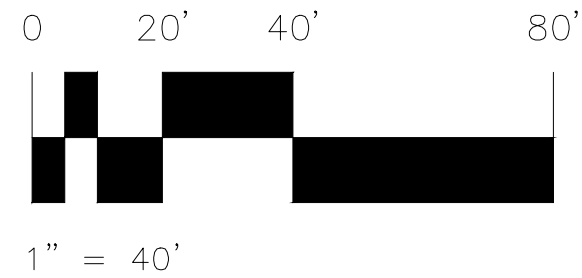


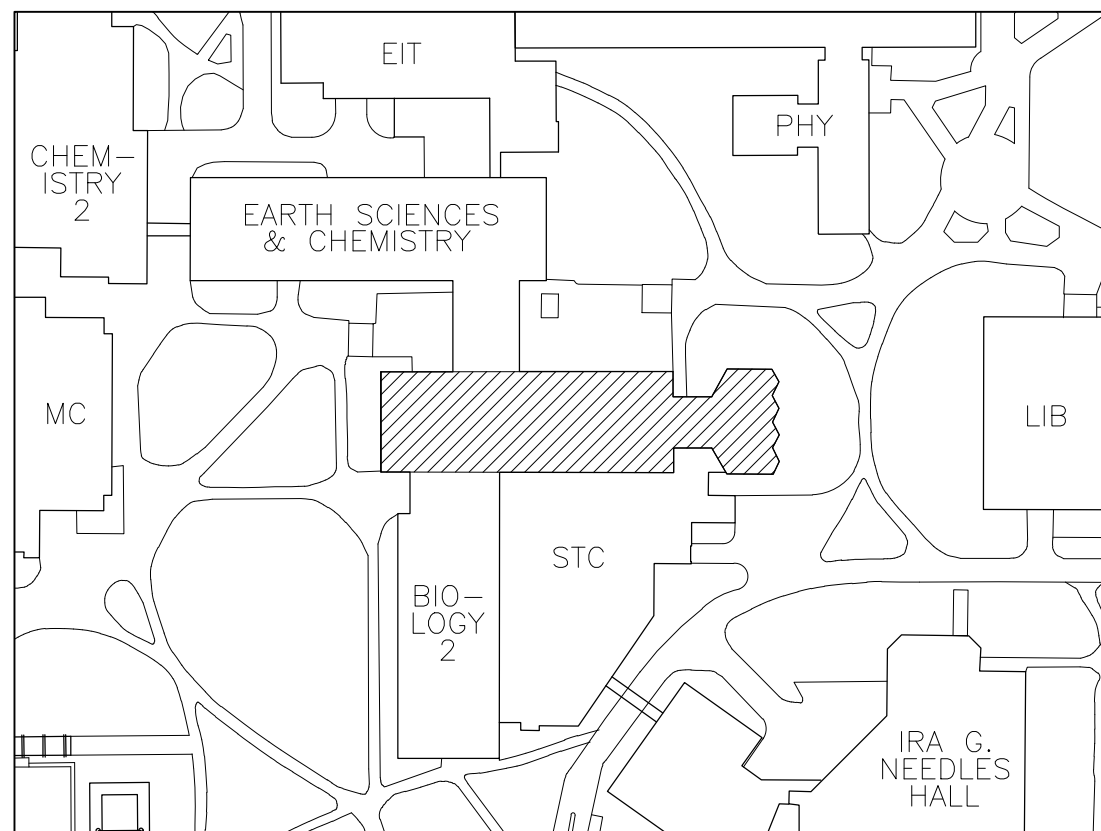

LEGEND

- M – MENS WASHROOM
- W – WOMENS WASHROOM
- A – ALL GENDER WASHROOM
- S – SINGLE USE WASHROOM
- ELV – ELEVATOR

THIRD FLOOR PLAN

BIOLOGY 1

BUILDING No. 7

UNIVERSITY OF WATERLOO

UPDATED – MAY 2023