

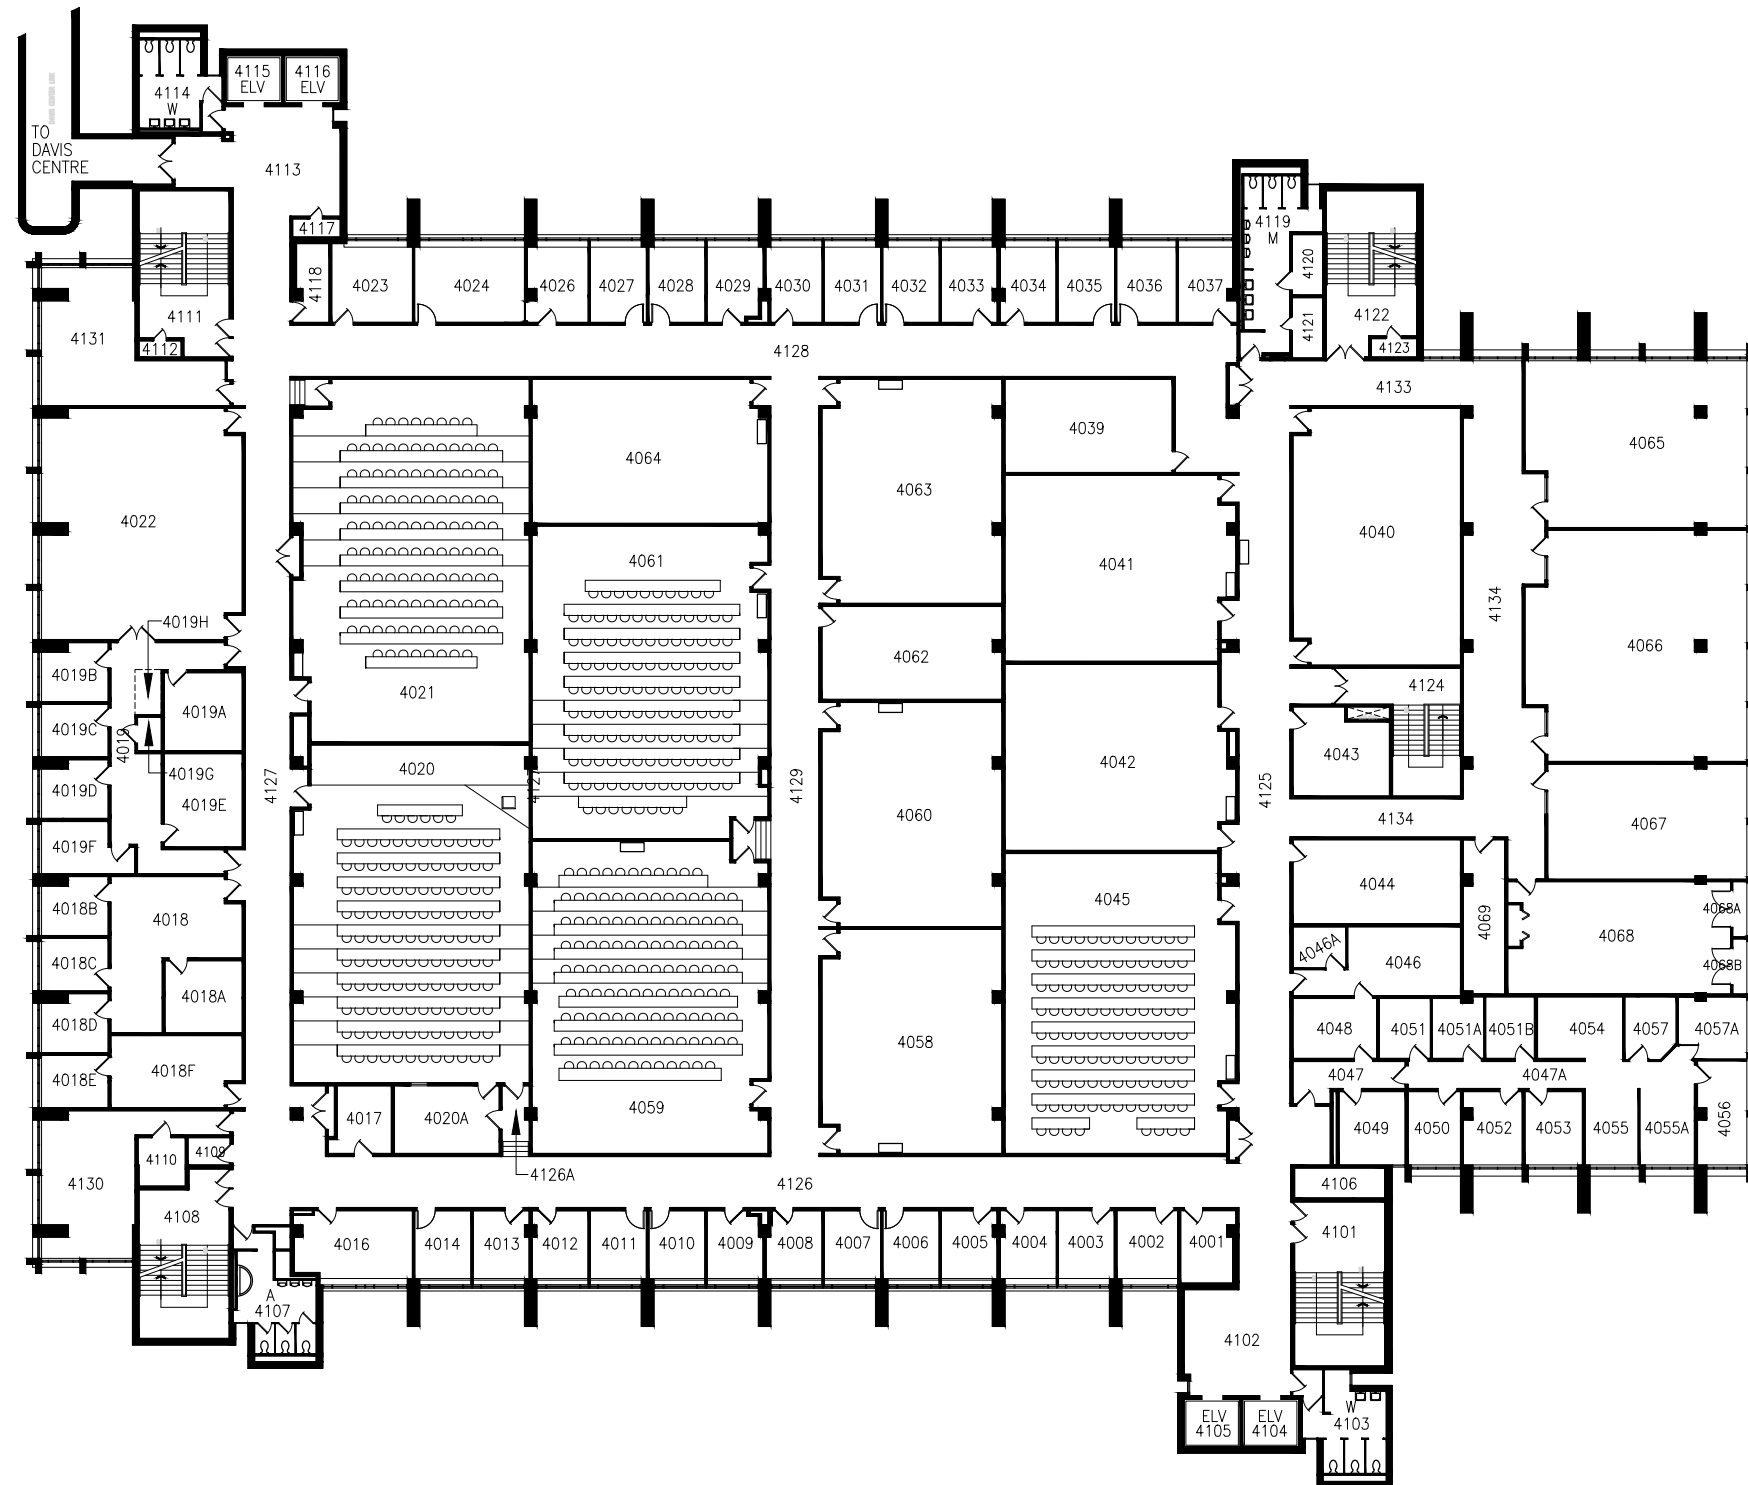
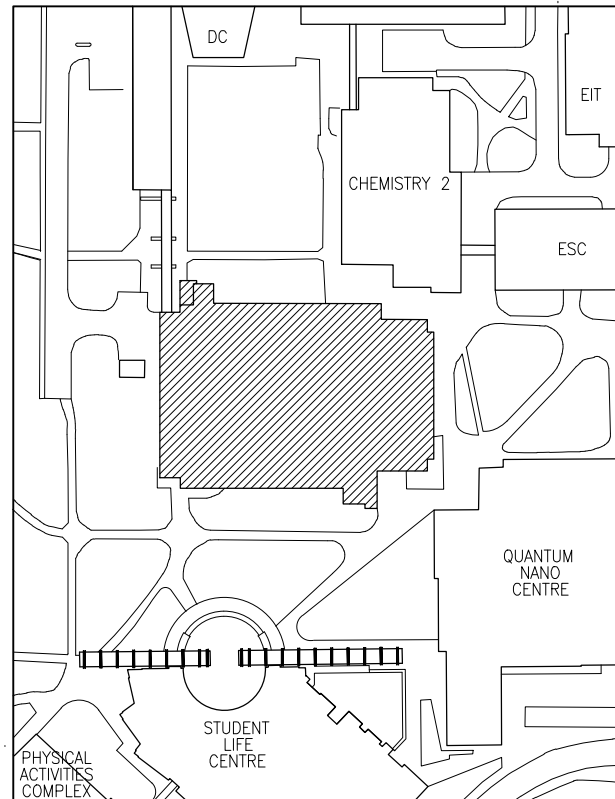


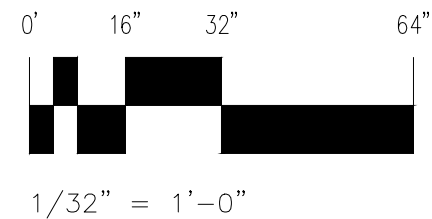

- LEGEND
- M - MENS WASHROOM
 - W - WOMENS WASHROOM
 - A - ALL GENDER WASHROOM
 - ELV - ELEVATOR

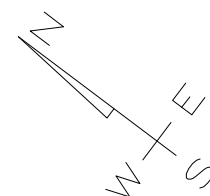

FOURTH FLOOR PLAN

MATHEMATICS AND COMPUTER

BUILDING No. 17

UNIVERSITY OF WATERLOO

UPDATED - DEC 2023